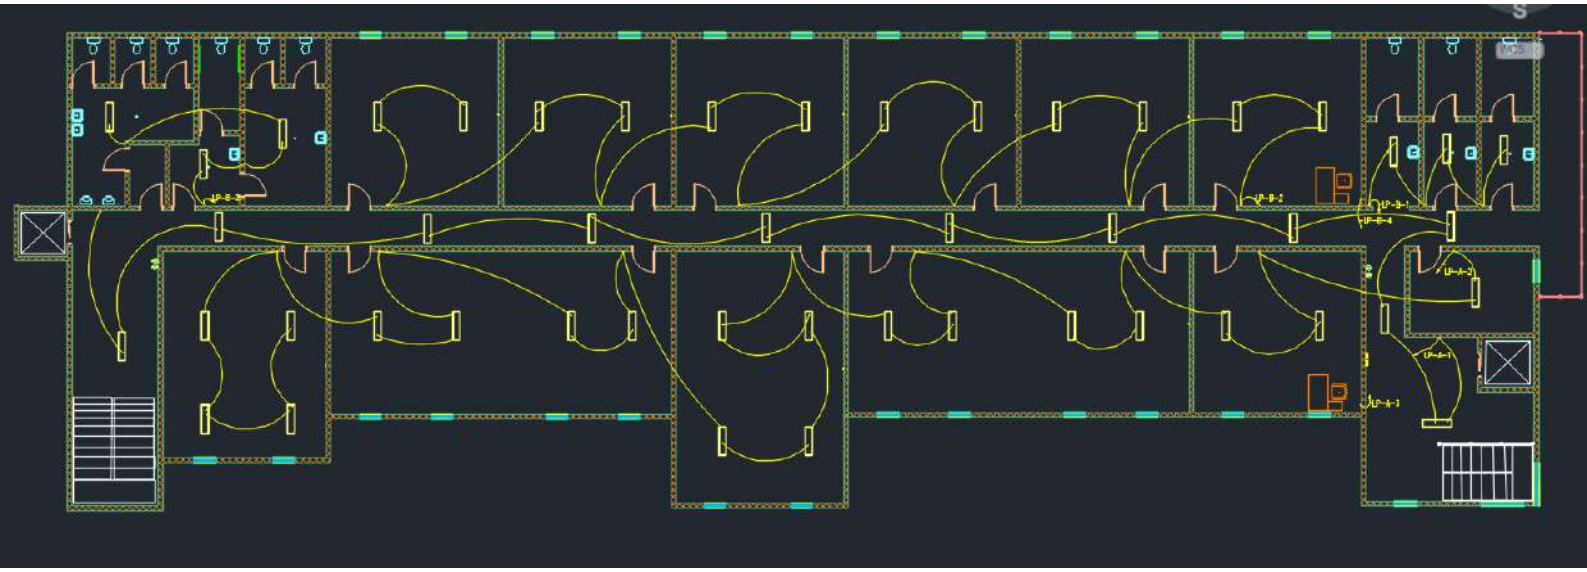

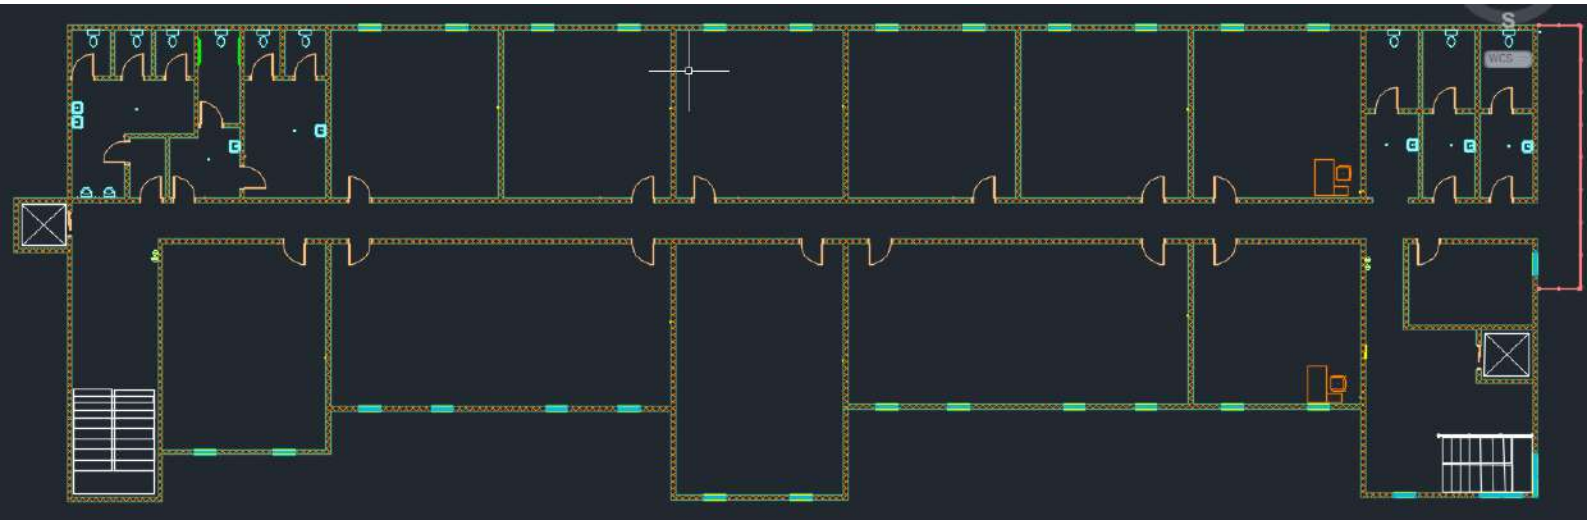
S
WCS

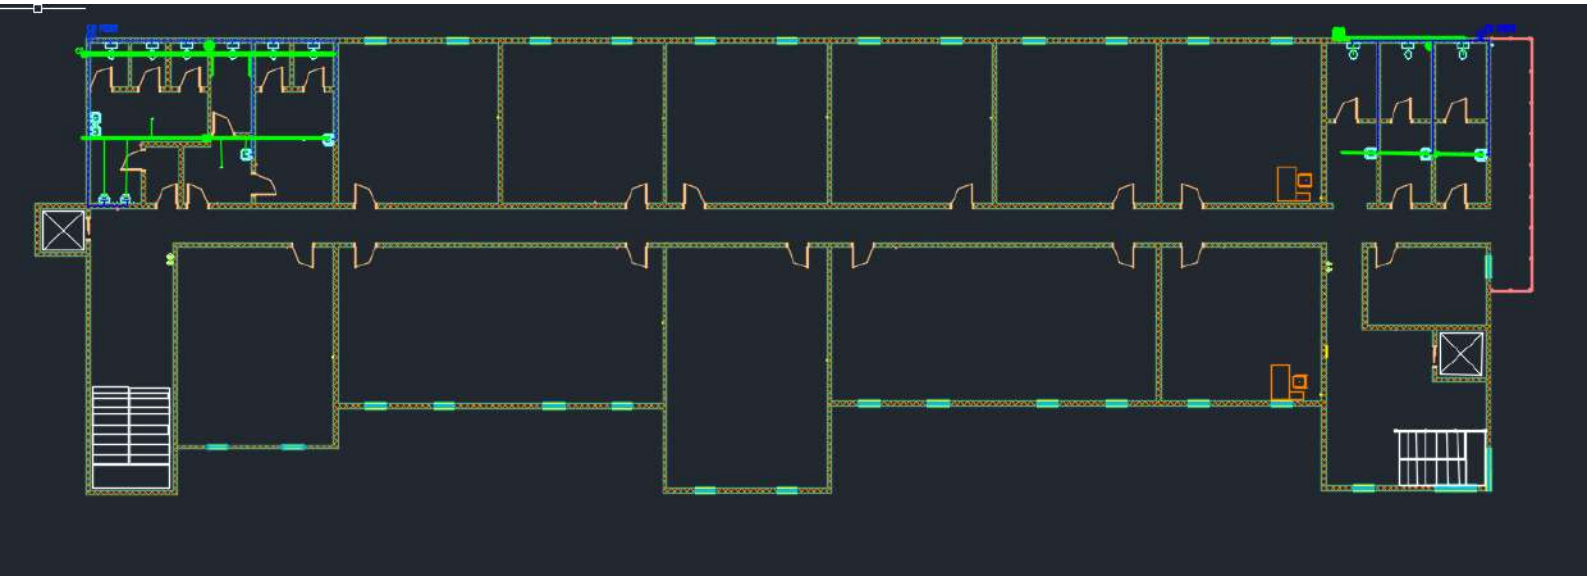

WATER AND PLUMBING

Cold Water Riser
(Water from Rooftop Tank)

Soil Stack/vent
(Down to Sewer,
Up to vent) 0.50mm

Waste Stack/vent
(Down to Sewer,
Up to Vent) 0.35mm

Water Pipe

Soil Pipe 0.50mm

Waste Pipe 0.35mm

CO Clean Out

Done.
Updating Indexes for block *Model_Space
Done.

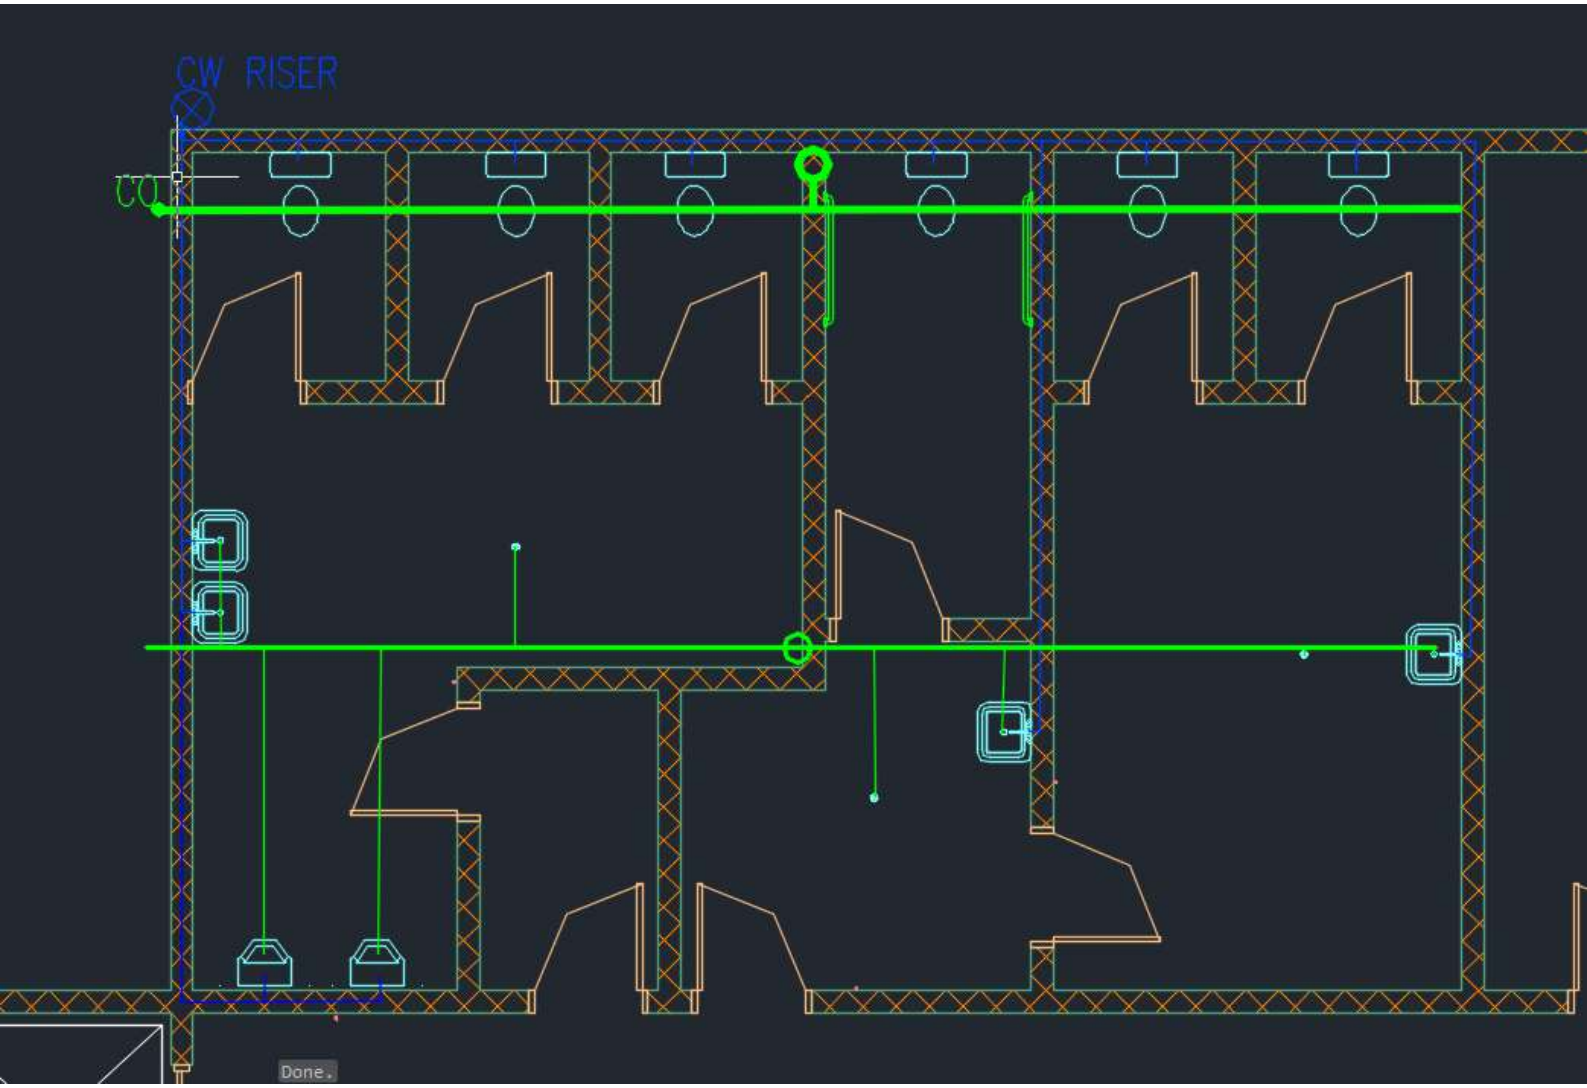
CW RISER
CO
Done.

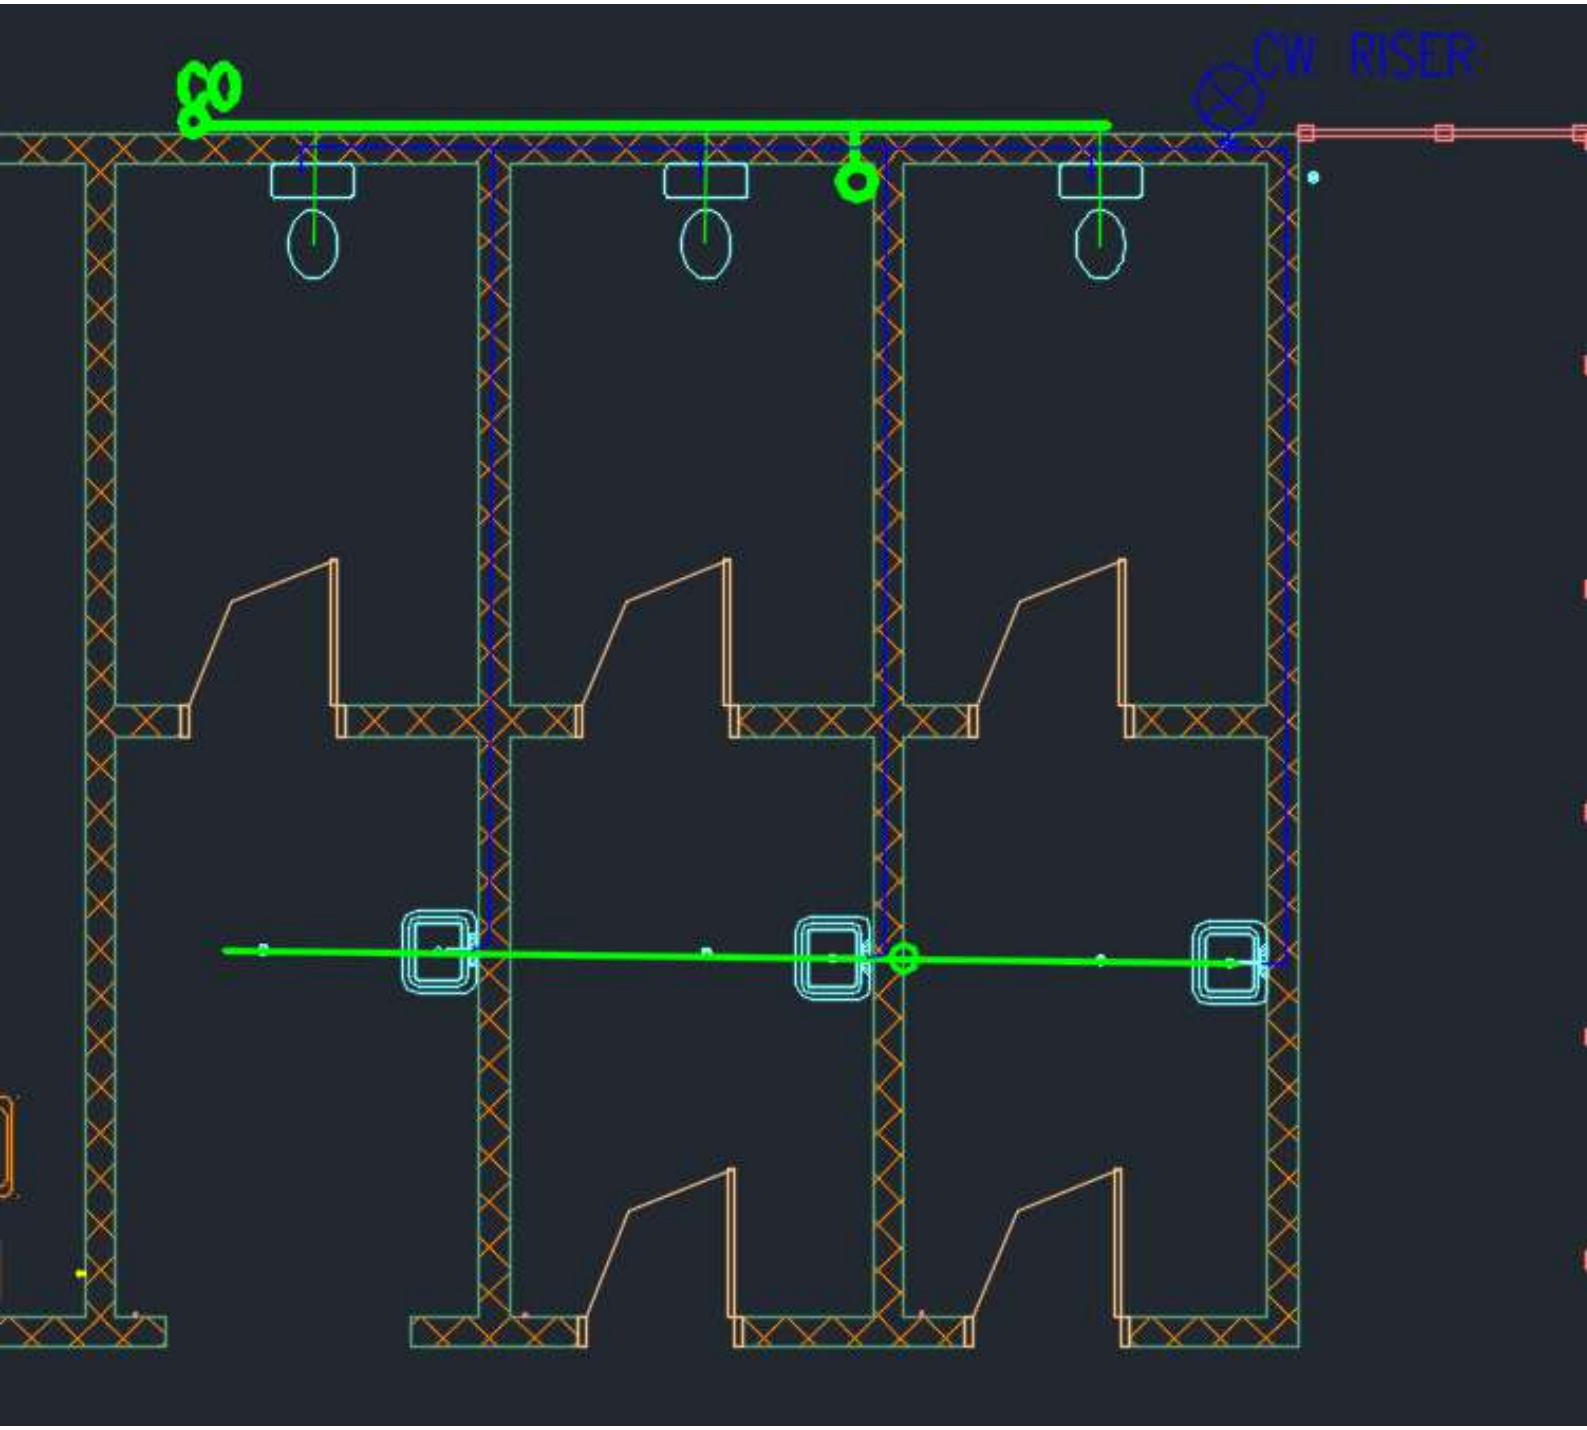
CW RISER

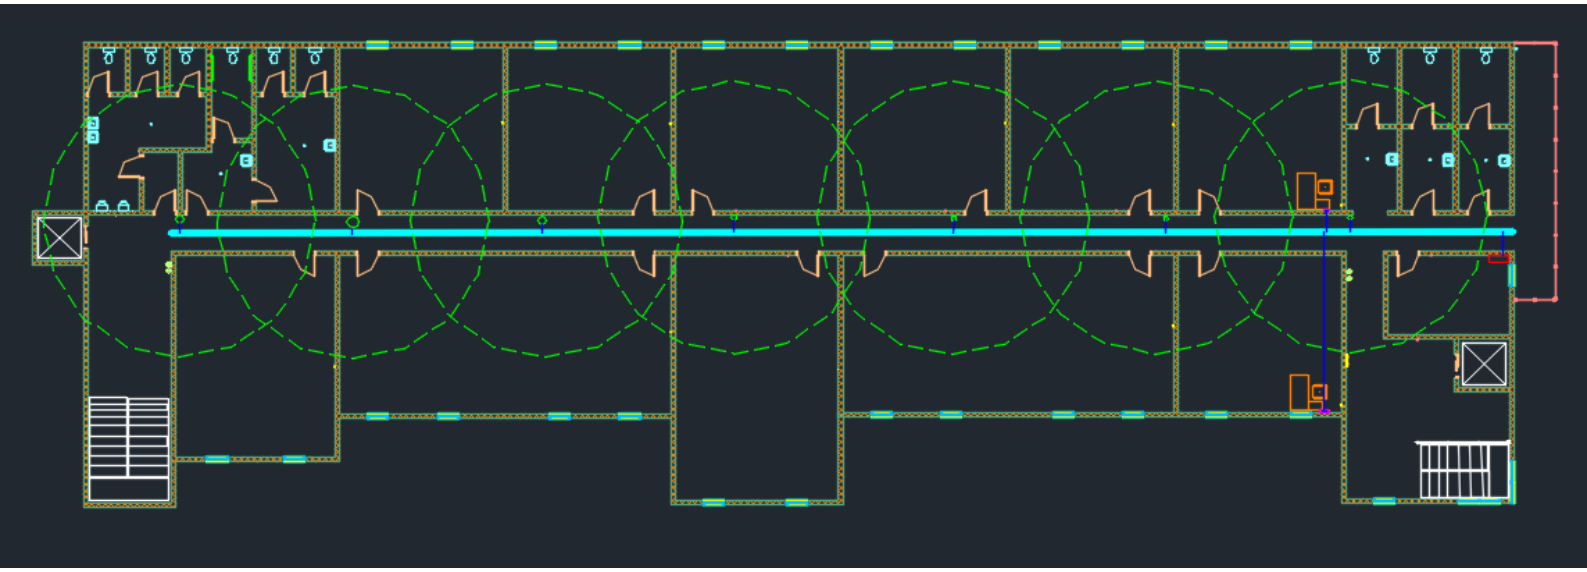

WIFI AND NETWORKING

Network Rack

Network Tray

Data Cable

Access Point

RJ45 Outlet

AP Range

ELECTRICAL AND WIRING

Wiring

Electrical Panel

Ceiling Light

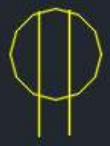

Wall Outlet

Single Pole Switch

2-Way Switch

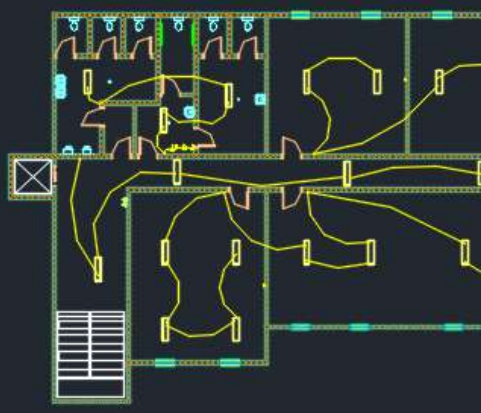

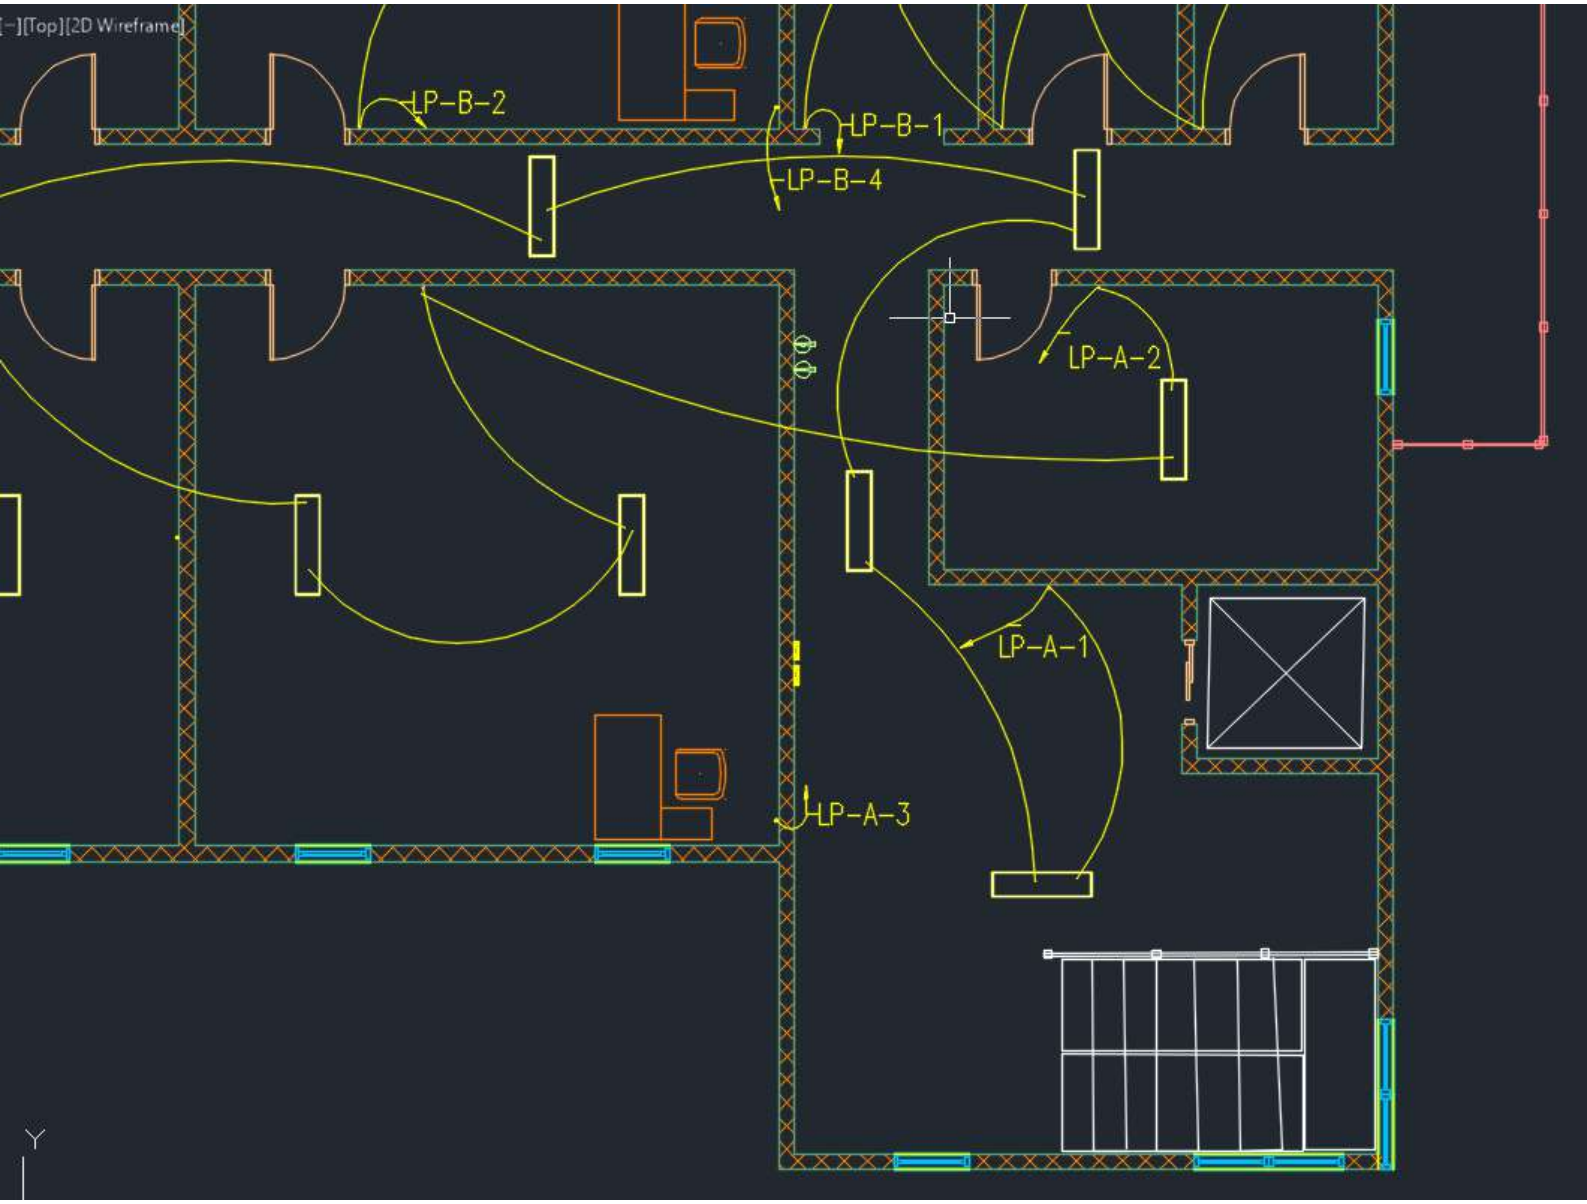
[-][Top][2D Wireframe]
LP-B-2
LP-B-1
LP-B-4
LP-A-2
LP-A-1
LP-A-3
Y